


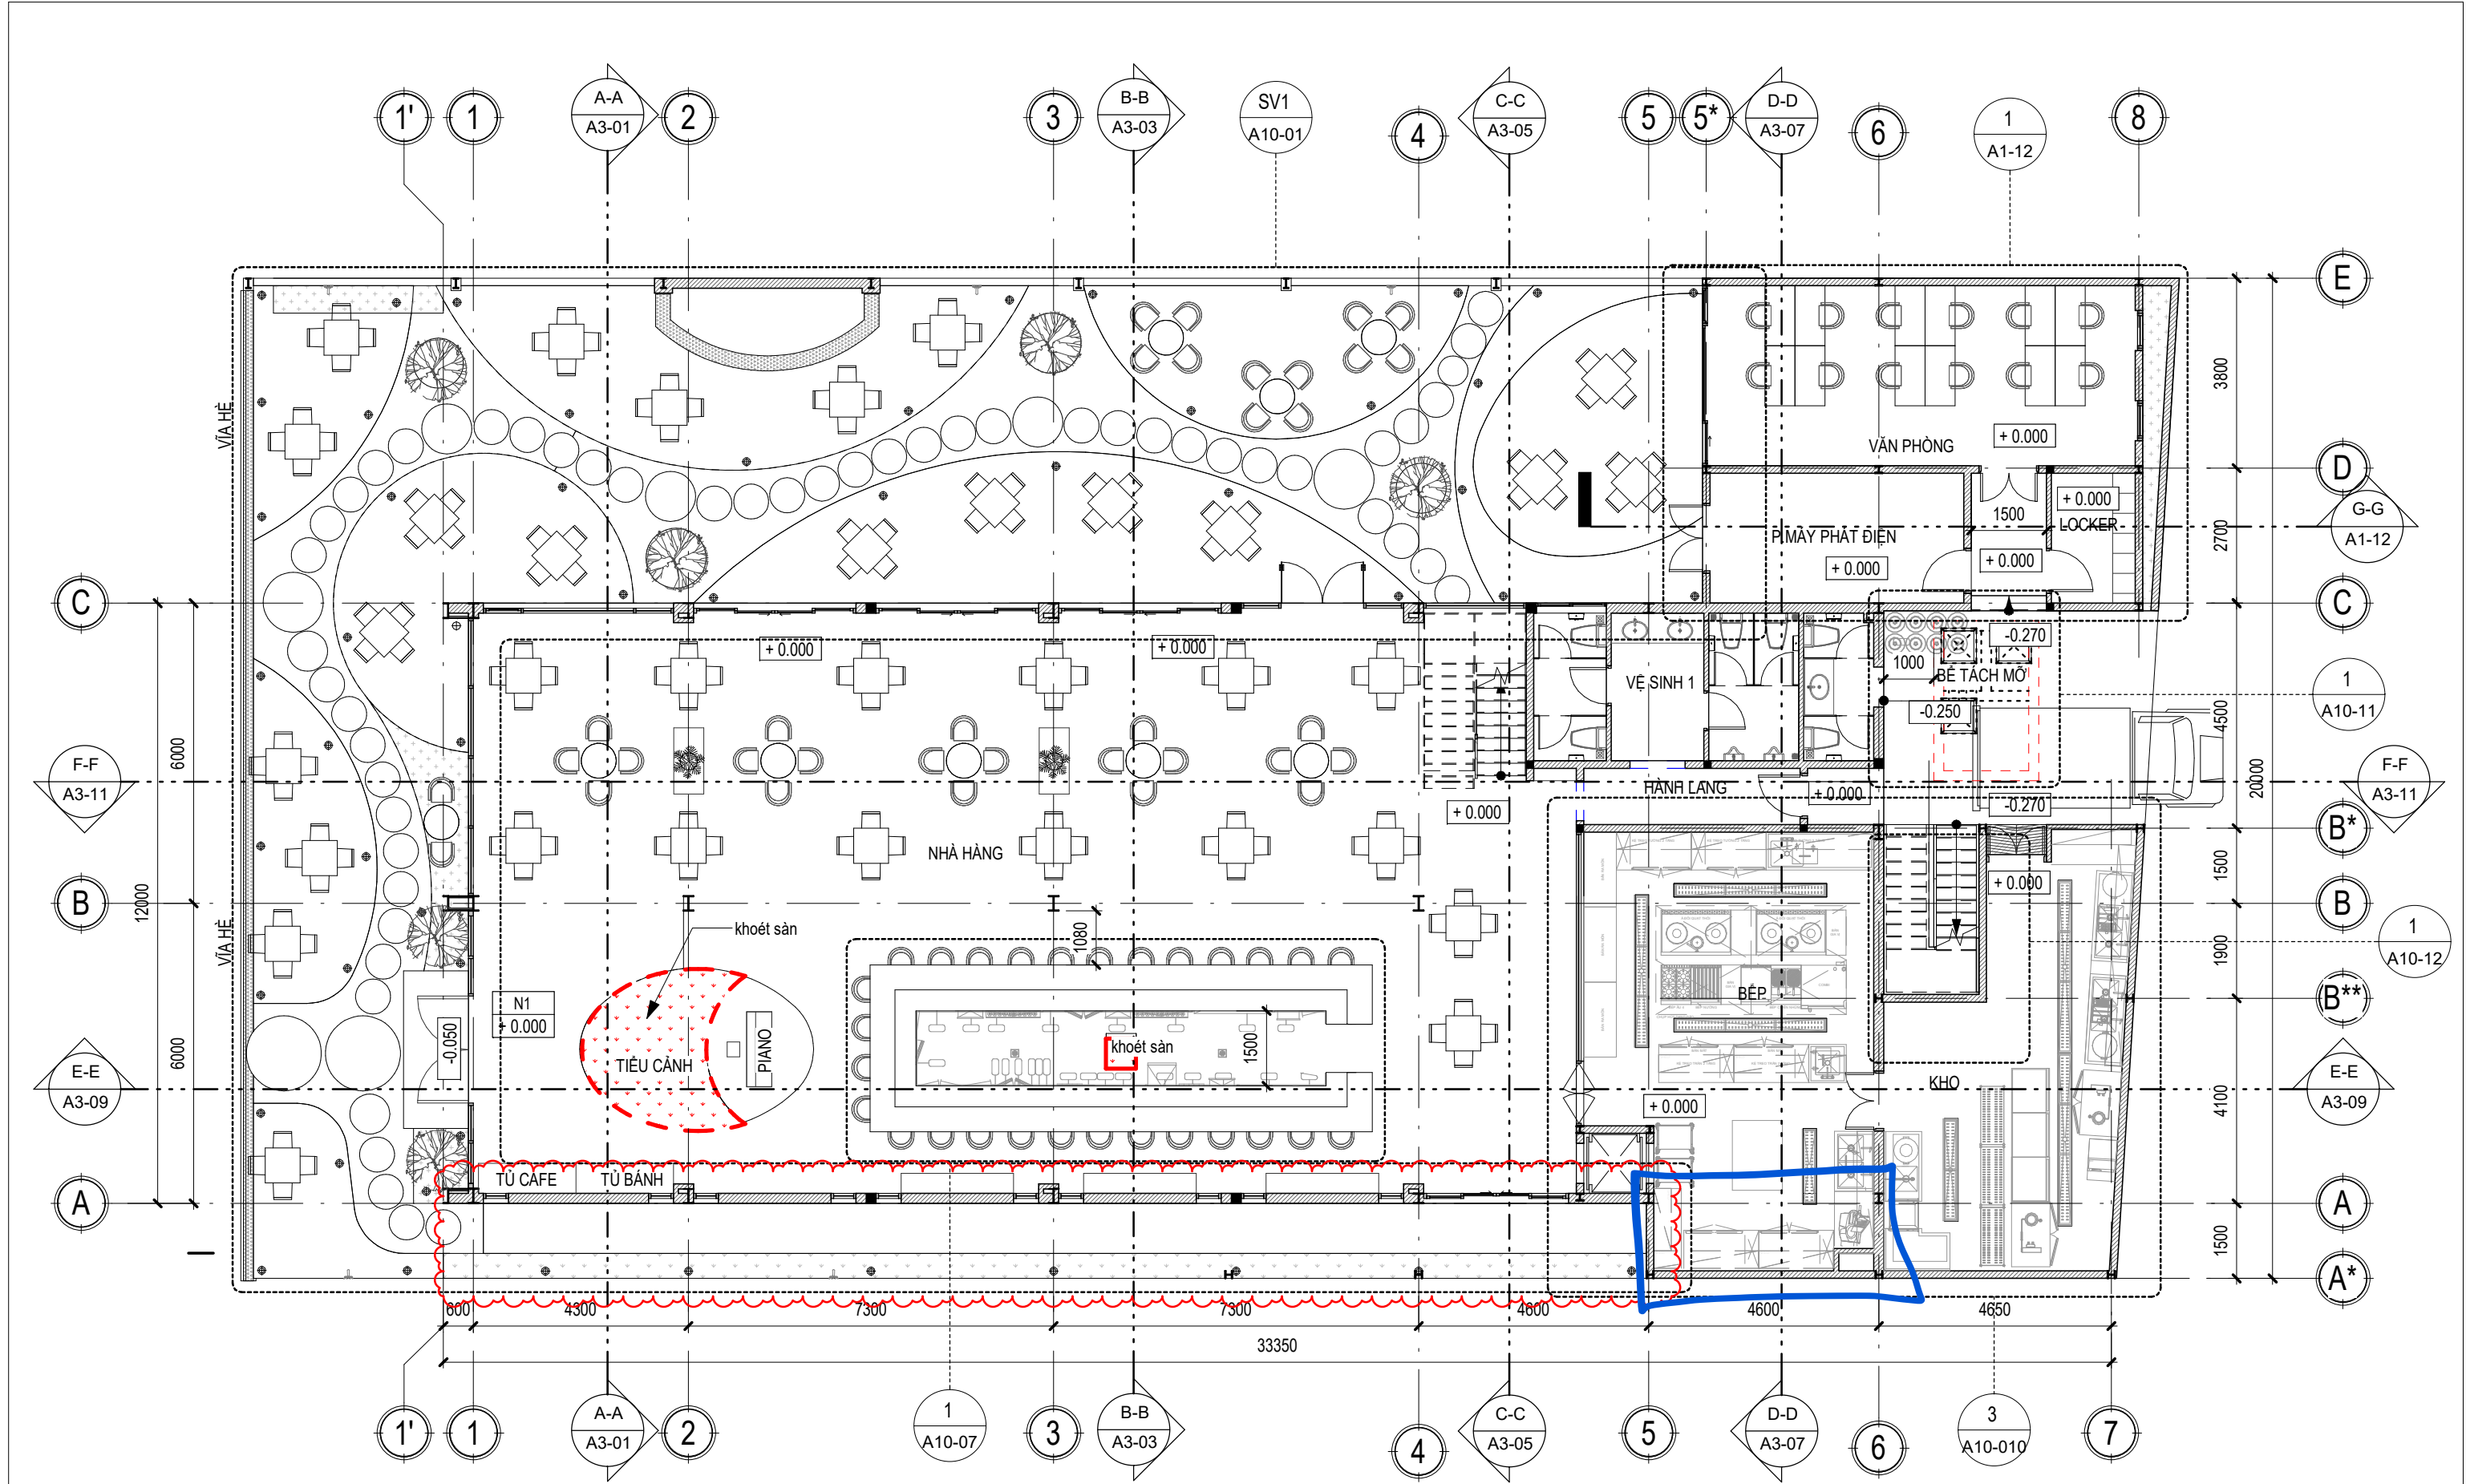

MỤC ĐÍCH PHÁT HÀNH/ ISSUED FOR	
THIẾT KẾ XIN PHÉP XÂY DỰNG	☒
THIẾT KẾ CƠ SỞ	☐
THIẾT KẾ KỸ THUẬT THI CÔNG	☐
THI CÔNG	☐
HOÀN CÔNG	☐
DỰ ÁN PROJECT NAME:	
WORKING SPACE BAR & DINNING	
ĐỊA ĐIỂM: THỦA ĐẤT SỐ 413 - TỜ BẢN ĐỒ SỐ 45, ĐƯỜNG TRẦN BẠCH ĐẰNG, PHƯỜNG AN HẢI, QUẬN SƠN TRÁ, THÀNH PHỐ ĐÀ NẴNG	


CHỦ ĐẦU TƯ	
CÔNG TY TNHH MIKA CASA	
KÝ HIỆU BẢN VẼ:	A1-02

VA Design 111 ĐOÀN NGỌC NHẠC - ĐÀ NẴNG thaithanhkts@gmail.com - 0902.482264	
GIÁM ĐỐC	NGUYỄN THÁI THÀNH


CHỦ NHIỆM/ PROJECTMANAGER	KTS. NGUYỄN THÁI THÀNH
KẾT CẤU/ DESIGNED	KS. TRẦN LONG PHI
MEP/ DESIGNED	KS. HỒ TRỌNG HIẾU
NỘI THẤT/ INTERIOR	KTS. HOÀNG DANH
TỔ PHỤ TRÁCH KỸ THUẬT THIẾT KẾ	

HẠNG MỤC - DRAWING TITLE:	KIẾN TRÚC
TÊN BẢN VẼ - DRAWING TITLE:	MẶT BẰNG TẦNG 1
GHI CHÚ CHUNG: + BẢN VẼ THỂ HIỆN LÀ MỘT PHẦN CỦA HỒ SƠ THIẾT KẾ, CẦN PHỐI HỢP VỚI CÁC BẢN VẼ KIẾN TRÚC, KẾT CẤU, ME LIÊN QUAN ĐỂ ĐỀ PHƯƠNG SỰ SAI KHÁC GIỮA CÁC BỘ MÔN THIẾT KẾ + ĐỂ TRÁNH SAI SÓT CẦN PHẢI KIỂM TRA KÍCH THƯỚC THỰC TẾ TRƯỚC KHI THI CÔNG + MỌI SỰ THAY ĐỔI CẦN PHẢI CÓ SỰ ĐỒNG Ý GIỮA BÊN A VÀ BÊN B TẠI CÔNG TRƯỜNG + KHÔNG SẠO CHÉP HOẶC TÀI SỬ DỤNG 1 PHẦN HỒ SƠ THIẾT KẾ KHI CHƯA CÓ SỰ ĐỒNG Ý CỦA ĐƠN VỊ THIẾT KẾ	

NGÀY HIỆU CHỈNH	HIỆU CHỈNH	NỘI DUNG HIỆU CHỈNH	KÝ DUYỆT
00			
01			
02			
03			
04			
05			
NGÀY PHÁT HÀNH			TỶ LỆ
ĐIỀU CHỈNH			
		VA design	A

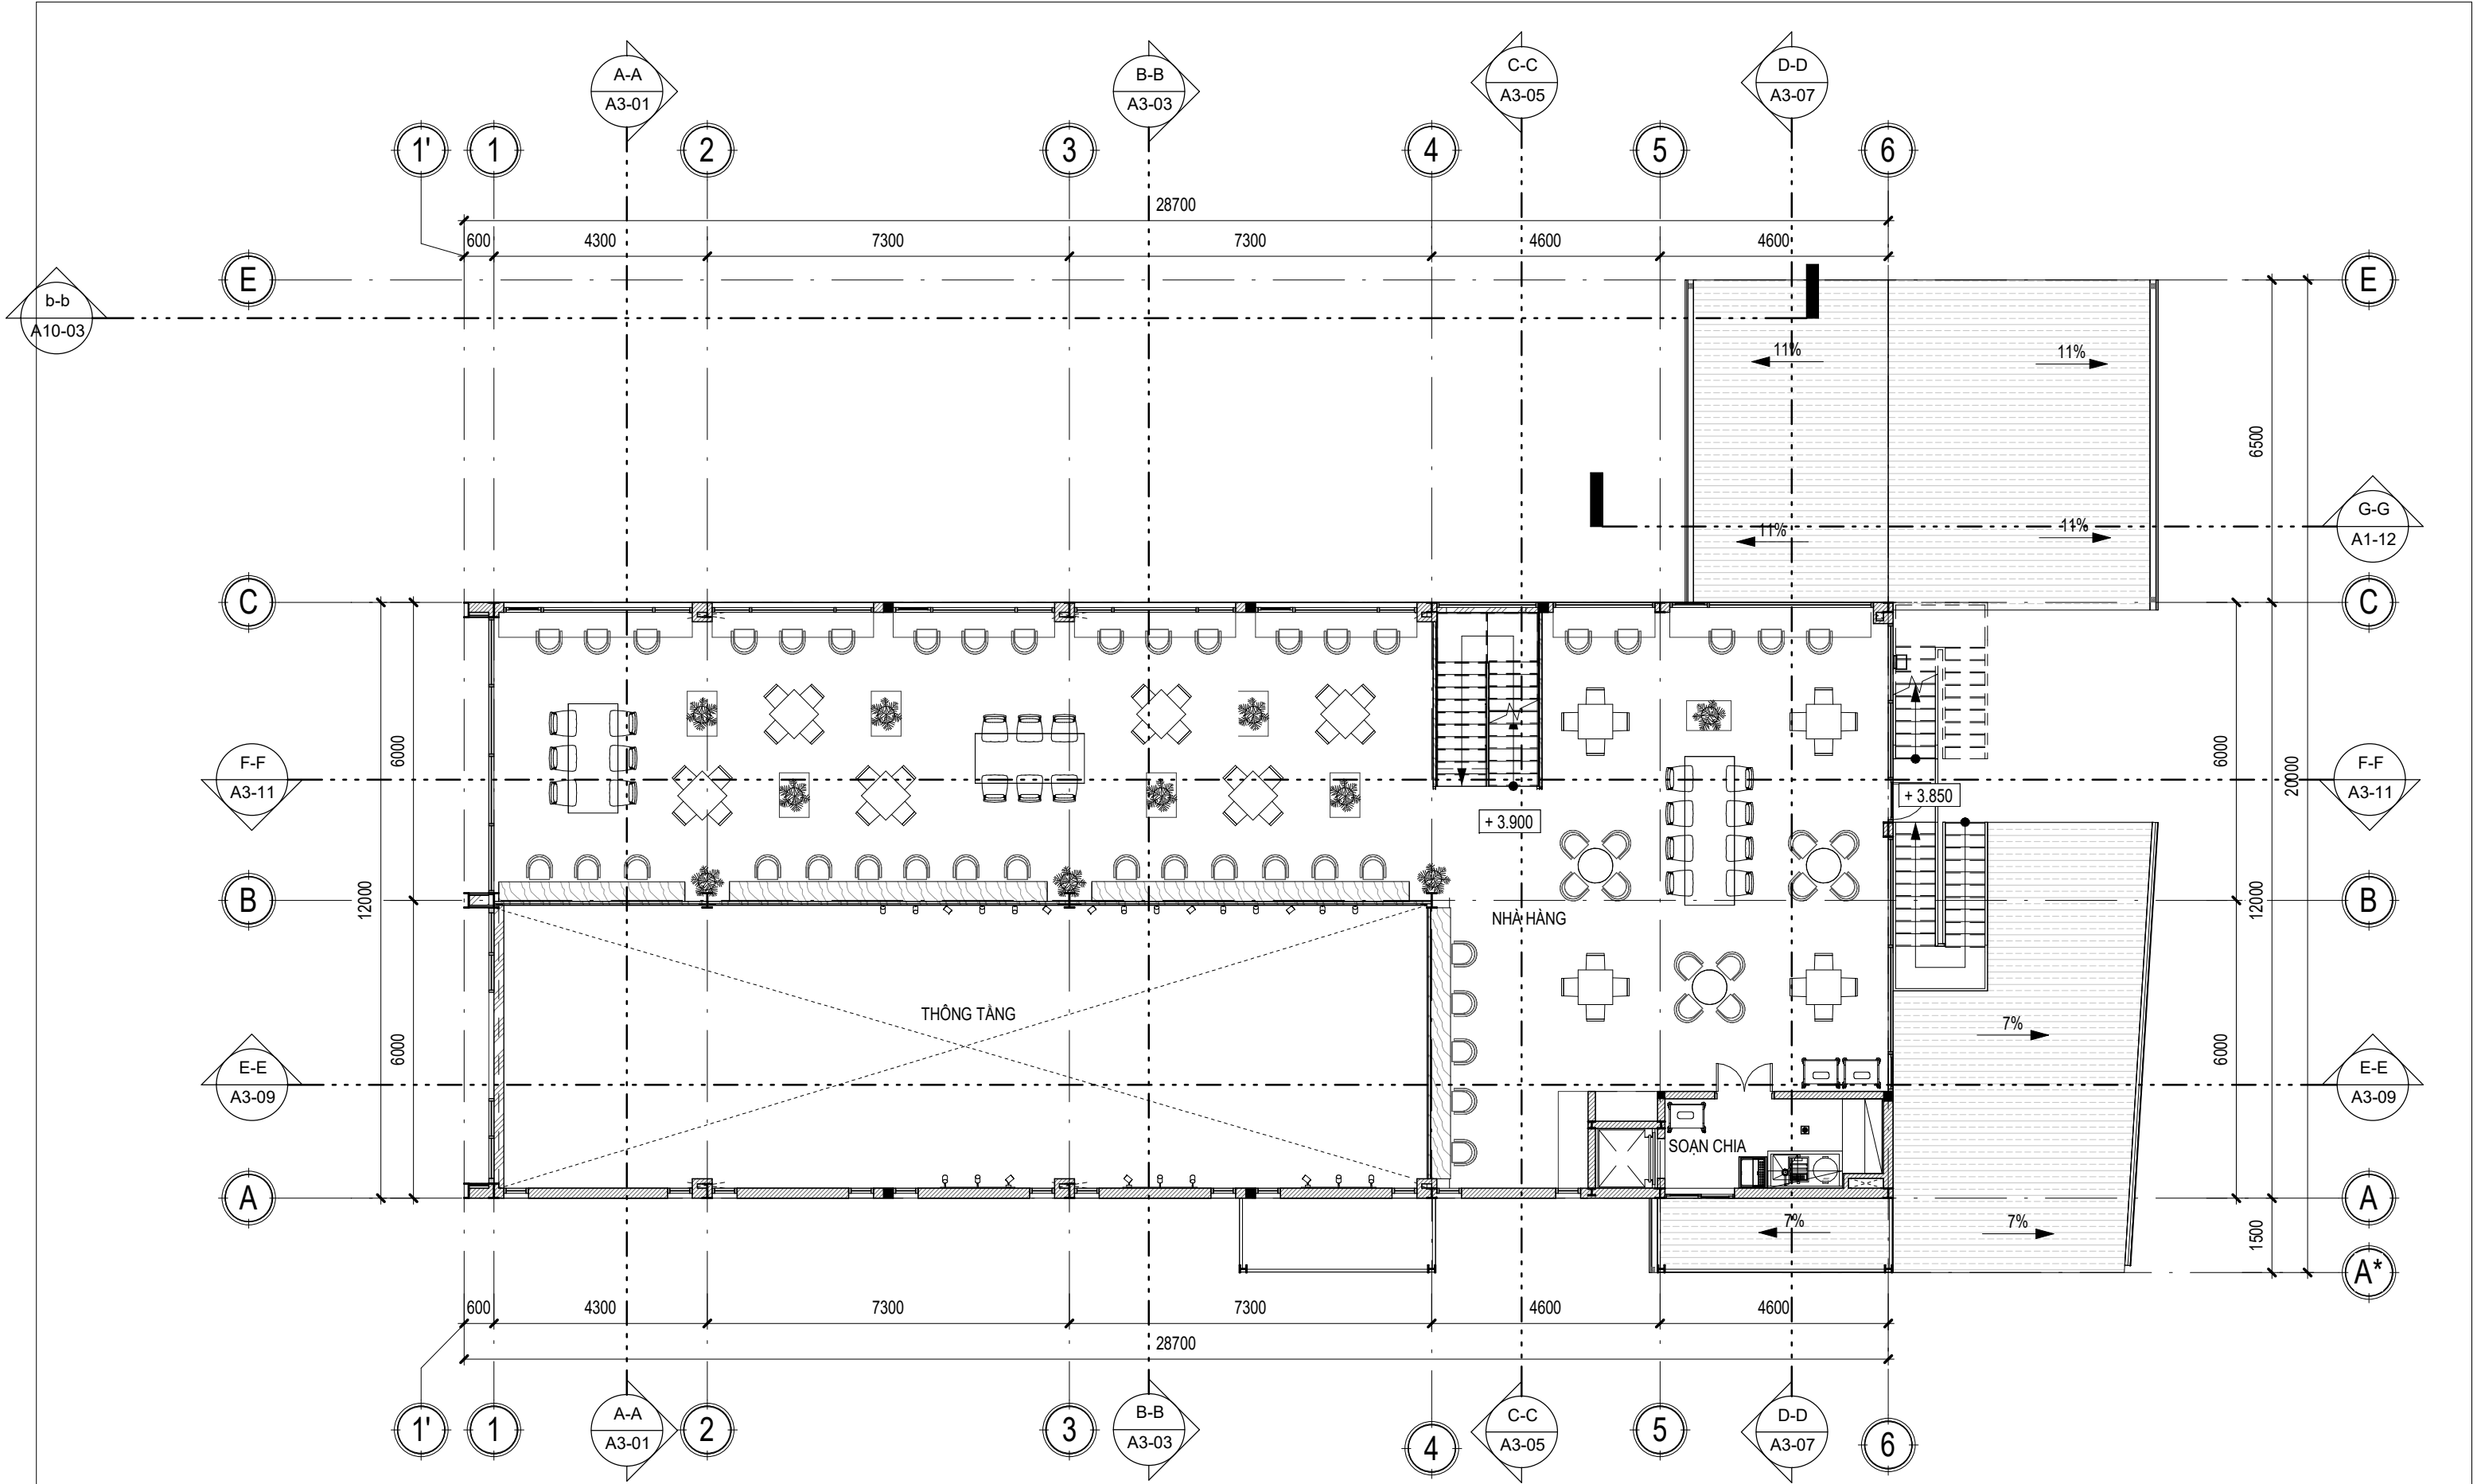

MỤC ĐÍCH PHÁT HÀNH/ ISSUED FOR		CHỦ ĐẦU TƯ	CÔNG TY TNHH MIKA CASA	VA Design 111 ĐOÀN NGỌC NHẠC - ĐÀ NẴNG thaitanhkts@gmail.com - 0902.482264	CHỦ NHIỆM/ PROJECTMANAGER	KTS. NGUYỄN THÁI THÀNH	HẠNG MỤC - DRAWING TITLE: KIẾN TRÚC	NGÀY HIỆU CHỈNH	HIỆU CHỈNH	NỘI DUNG HIỆU CHỈNH	KÝ DUYỆT
THIẾT KẾ XIN PHÉP XÂY DỰNG	☒				KẾT CẤU/ DESIGNED	KS. TRẦN LONG PHI	TÊN BẢN VẼ - DRAWING TITLE: MẶT BẰNG TẦNG 2 GHI CHÚ CHUNG: + BẢN VẼ THỂ HIỆN LÀ MỘT PHẦN CỦA HỒ SƠ THIẾT KẾ. CẦN PHỐI HỢP VỚI CÁC BẢN VẼ KIẾN TRÚC, KẾT CẤU, ME LIÊN QUAN ĐỂ ĐỀ PHÒNG SỰ SAI KHÁC GIỮA CÁC BỘ MÔN THIẾT KẾ + ĐỂ TRÁNH SAI SÓT CẦN PHẢI KIỂM TRA KÍCH THƯỚC THỰC TẾ TRƯỚC KHI THI CÔNG + MỌI SỰ THAY ĐỔI CẦN PHẢI CÓ SỰ ĐỒNG Ý GIỮA BÊN A VÀ BÊN B TẠI CÔNG TRƯỜNG + KHÔNG SAO CHÉP HOẶC TÁI SỬ DỤNG 1 PHẦN HỒ SƠ THIẾT KẾ KHI CHƯA CÓ SỰ ĐỒNG Ý CỦA ĐƠN VỊ THIẾT KẾ	00			
THIẾT KẾ CƠ SỞ	☐				MEP/ DESIGNED	KS. HỒ TRỌNG HIẾU		01			
THIẾT KẾ KỸ THUẬT THI CÔNG	☐				NỘI THẤT/ INTERIOR	KTS. HOÀNG DANH		02			
THI CÔNG	☐							03			
HOÀN CÔNG	☐							04			
DỰ ÁN/ PROJECT NAME:		KÝ HIỆU BẢN VẼ:	A1-03	GIÁM ĐỌC	NGUYỄN THÁI THÀNH	TỔ PHỤ TRÁCH KỸ THUẬT THIẾT KẾ	05				
WORKING SPACE BAR & DINNING							NGÀY PHÁT HÀNH		TỶ LỆ		
ĐỊA ĐIỂM : THỦA ĐẤT SỐ 413 - TỜ BẢN ĐỒ SỐ 45, ĐƯỜNG TRẦN BẠCH ĐĂNG, PHƯỜNG AN HẢI, QUẬN SƠN TRÁ, THÀNH PHỐ ĐÀ NẴNG							ĐIỀU CHỈNH				
								VAdesign		A	

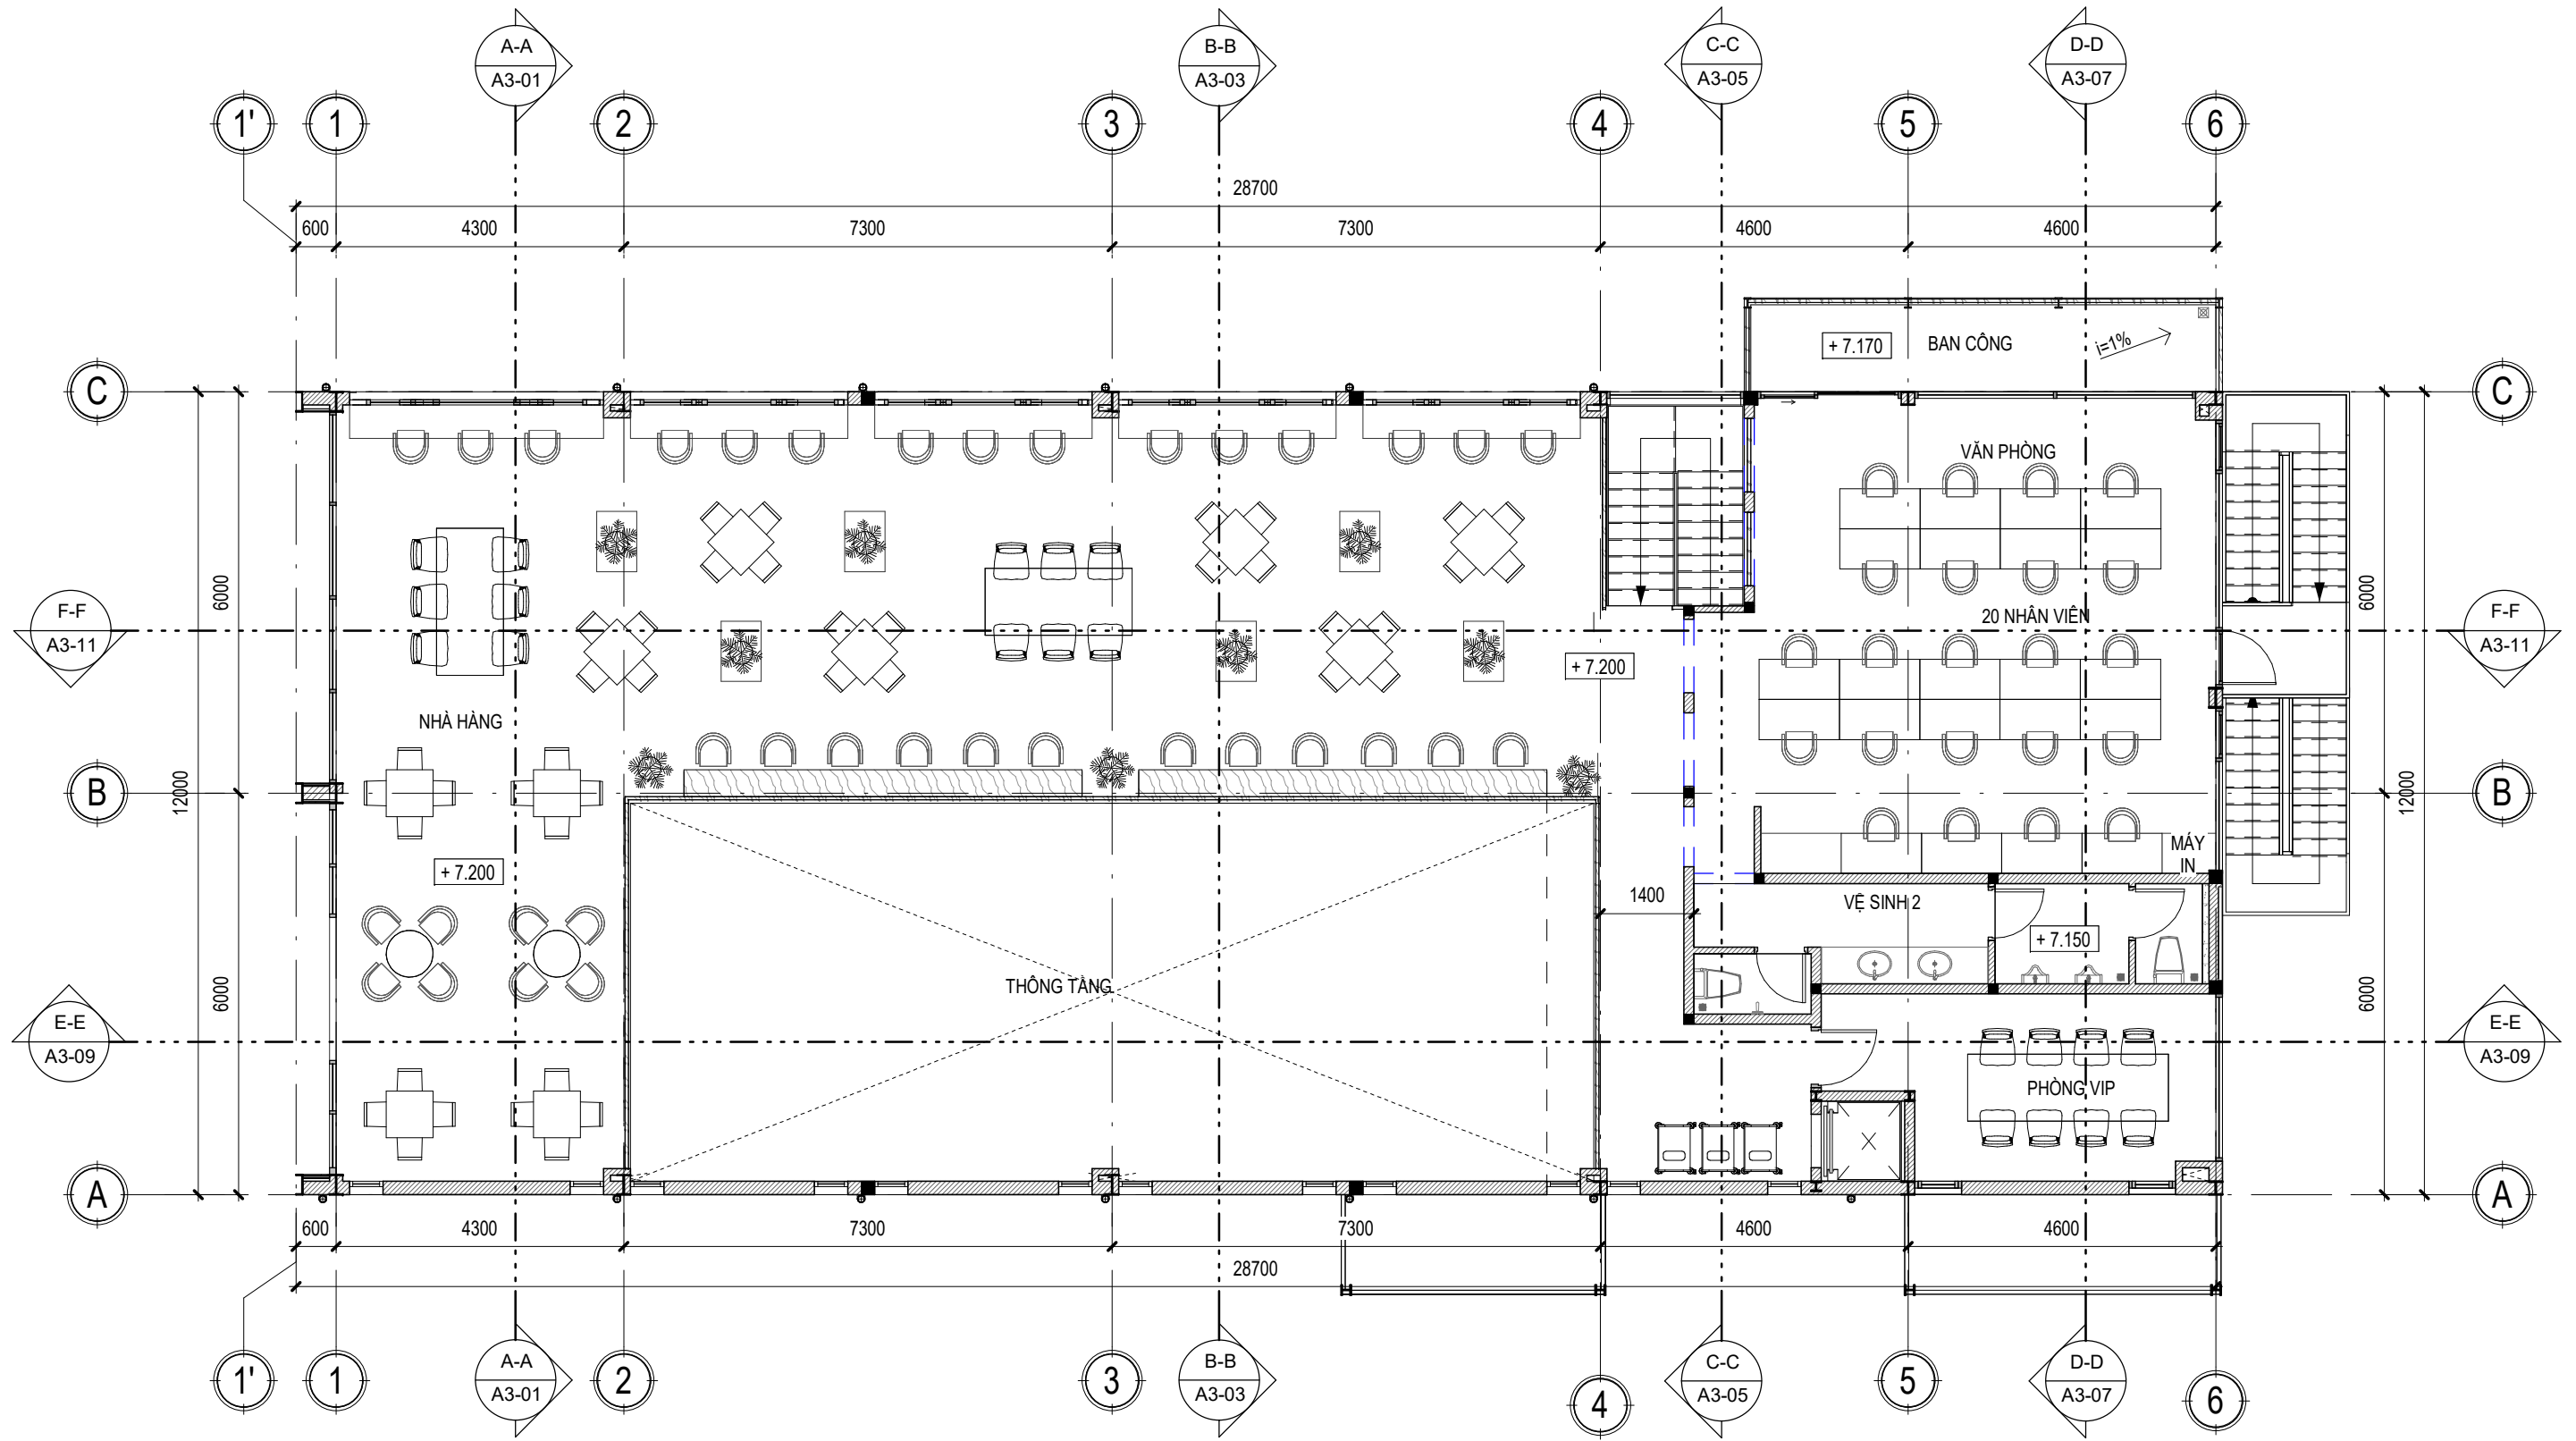

MỤC ĐÍCH PHÁT HÀNH/ ISSUED FOR		CHỦ ĐẦU TƯ		VA Design 111 ĐOÀN NGỌC NHẠC - ĐÀ NẴNG thaithanhkts@gmail.com - 0902.482264	CHỦ NHIỆM/ PROJECTMANAGER		KTS. NGUYỄN THÁI THÀNH	Hand	HẠNG MỤC - DRAWING TITLE:		KIẾN TRÚC		NGÀY	HIỆU CHỈNH	NỘI DUNG HIỆU CHỈNH		KÝ DUYỆT
THIẾT KẾ XIN PHÉP XÂY DỰNG		☒			KẾT CẤU/ DESIGNED		KS. TRẦN LONG PHI	Trần	TÊN BẢN VẼ - DRAWING TITLE:		MẶT BẰNG TẦNG 3		00				
THIẾT KẾ CƠ SỞ		☐			MEP/ DESIGNED		KS. HỒ TRỌNG HIẾU	Ho	GHI CHÚ CHUNG: + BẢN VẼ THỂ HIỆN LÀ MỘT PHẦN CỦA HỒ SƠ THIẾT KẾ. CẦN PHỐI HỢP VỚI CÁC BẢN VẼ KIẾN TRÚC, KẾT CẤU, ME LIÊN QUAN ĐỂ ĐỀ PHÒNG SỰ SAI KHÁC GIỮA CÁC BỘ MÔN THIẾT KẾ + ĐỂ TRÁNH SAI SÓT CẦN PHẢI KIỂM TRA KÍCH THƯỚC THỰC TẾ TRƯỚC KHI THI CÔNG + MỌI SỰ THAY ĐỔI CẦN PHẢI CÓ SỰ ĐỒNG Ý GIỮA BÊN A VÀ BÊN b TẠI CÔNG TRƯỜNG + KHÔNG SAO CHÉP HOẶC TÁI SỬ DỤNG 1 PHẦN HỒ SƠ THIẾT KẾ KHI CHƯA CÓ SỰ ĐỒNG Ý CỦA ĐƠN VỊ THIẾT KẾ		01						
THIẾT KẾ KỸ THUẬT THI CÔNG		☐			NỘI THẤT/ INTERIOR		KTS. HOÀNG ANH	Ha	02								
THI CÔNG		☐			TỔ PHỤ TRÁCH KỸ THUẬT THIẾT KẾ		NGUYỄN THÁI THÀNH		03								
HOÀN CÔNG		☐									04						
DỰ ÁN PROJECT NAME:		KÝ HIỆU BẢN VẼ:		GIÁM ĐỐC				05					NGÀY PHÁT HÀNH		TỶ LỆ		
WORKING SPACE BAR & DINNING		A1-04		NGUYỄN THÁI THÀNH				06					ĐIỀU CHỈNH				
ĐỊA ĐIỂM : THỦA ĐẤT SỐ 413 - TỜ BẢN ĐỒ SỐ 45, ĐƯỜNG TRẦN BẠCH ĐĂNG, PHƯỜNG AN HẢI, QUẬN SƠN TRÁ, THÀNH PHỐ ĐÀ NẴNG														VAdesign		A	

